
## LINHA: 6"-VP-1001-B1A-HC

DE: V-101 (BOCAL N3)  PARA: LINHA 6"-VP-1002

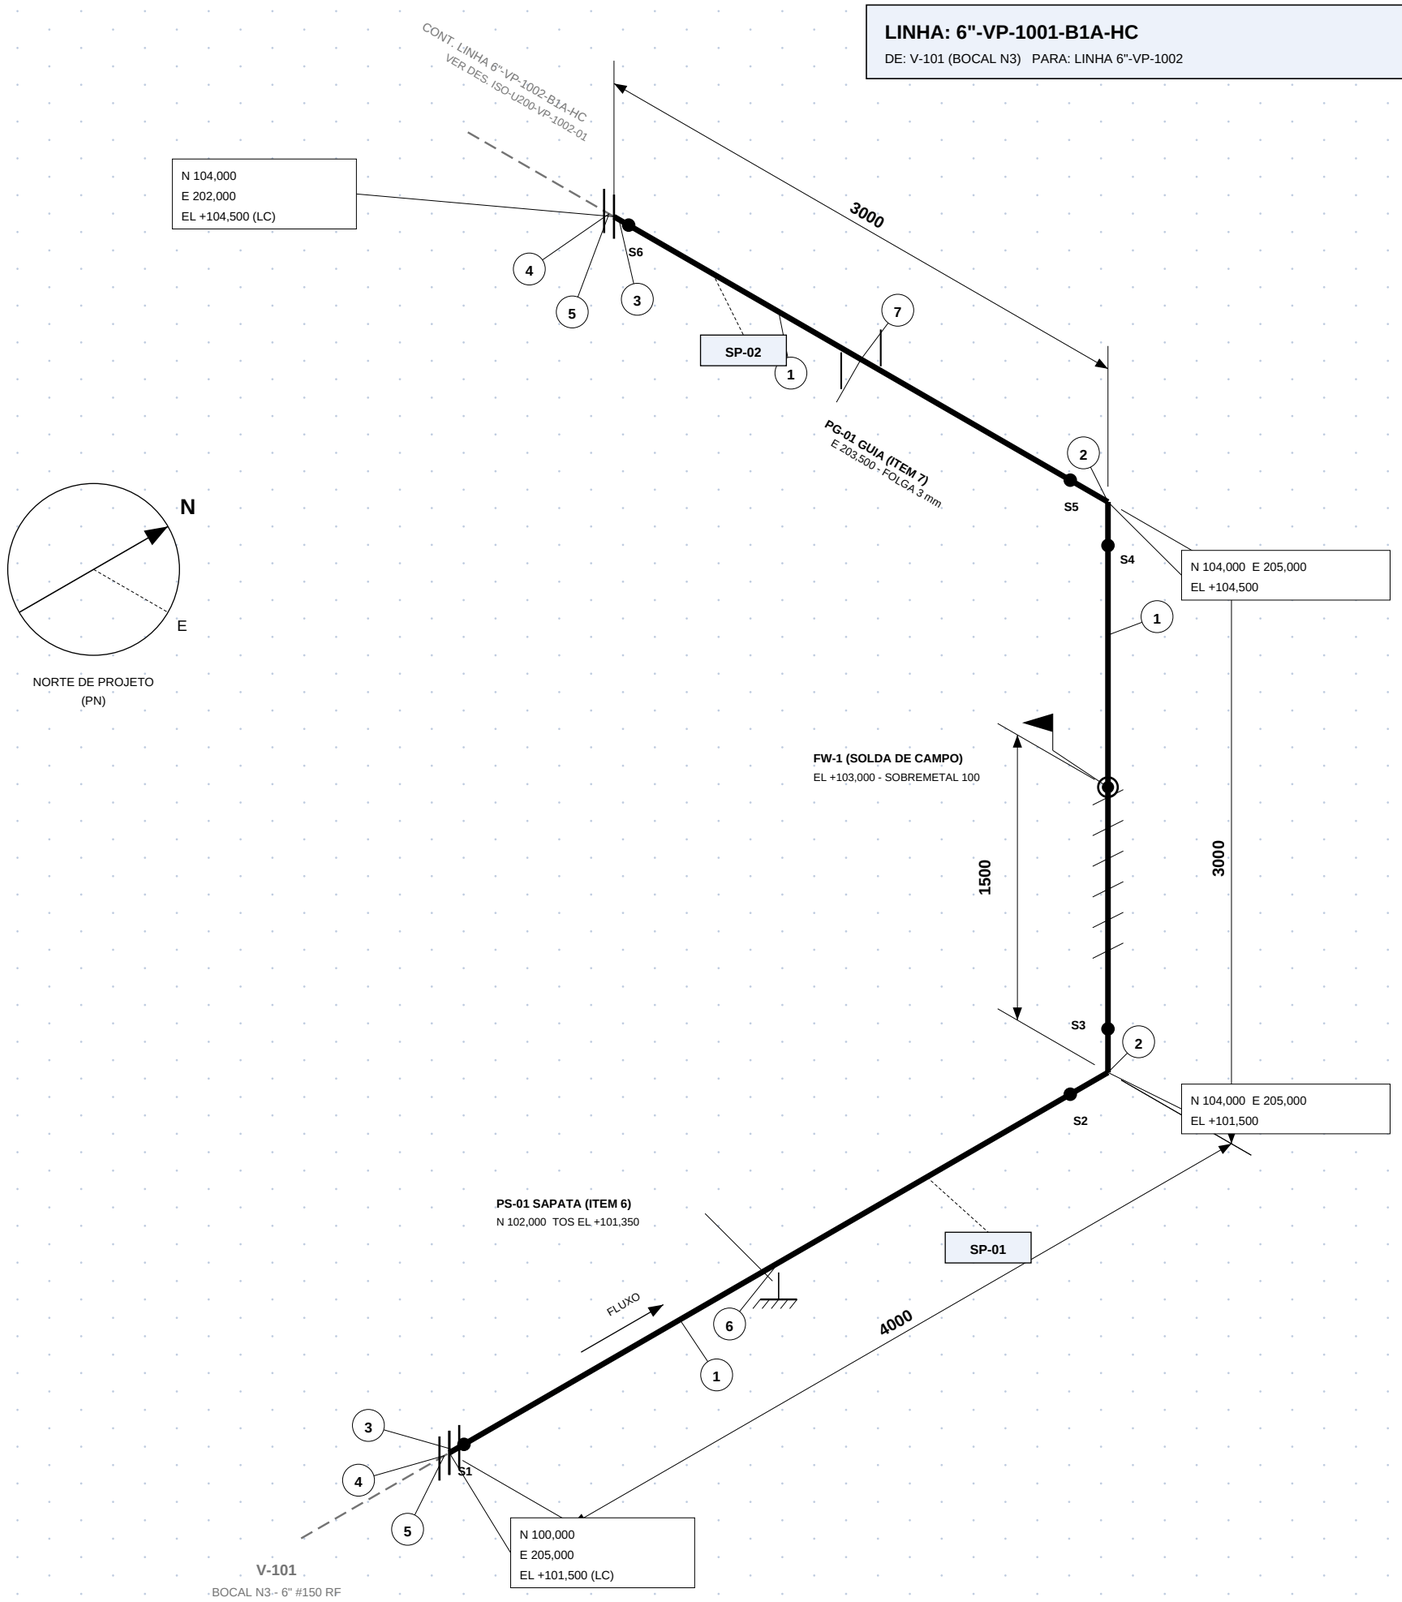


*DESENHO SEM ESCALA*

### LISTA DE MATERIAIS

| IT | DESCRIÇÃO | NORMA / MATERIAL | QTD |
|---|---|---|---|
| **MATERIAL DE FABRICAÇÃO (SPOOLS)** | | | |
| 1 | TUBO 6" SCH 40 (e=7,11) PB, S/ COSTURA | ASME B36.10 / A106 Gr.B | 9,0 m |
| 2 | CURVA 90° RL 6" SCH 40, SOLDA TOPO | ASME B16.9 / A234 WPB | 2 pç |
| 3 | FLANGE WN 6" #150 RF SCH 40 | ASME B16.5 / A105 | 2 pç |
| **MATERIAL DE MONTAGEM** | | | |
| 4 | JUNTA ESPIRAL 6" #150 304/GRAF. C/ ANEL | ASME B16.20 | 2 pç |
| 5 | ESTOJO 3/4" x 4.1/2" C/ 2 PORCAS SEXT. | A193 B7 / A194 2H | 16 pç |
| **SUPORTES** | | | |
| 6 | SAPATA PS-01 P/ TUBO 6" (H=150) | PADRÃO SUP-01 / A36 | 1 cj |
| 7 | GUIA PG-01 P/ TUBO 6" | PADRÃO SUP-05 / A36 | 1 cj |

**PESO ESTIMADO (S/ ISOLAMENTO): ~ 300 kg**

### LISTA DE CORTE - TUBO ITEM 1

| PÇ | TRECHO | SPOOL | COMP. (mm) |
|---|---|---|---|
| C1 | S1 - S2 (FLANGE / CURVA, SENT. NORTE) | SP-01 | 3682 |
| C2 | S3 - FW-1 (VERTICAL INFERIOR) | SP-01 | 1271 + 100 |
| C3 | FW-1 - S4 (VERTICAL SUPERIOR) | SP-02 | 1271 |
| C4 | S5 - S6 (CURVA / FLANGE, SENT. OESTE) | SP-02 | 2682 |

### CONDIÇÕES DE PROCESSO E PROJETO

| PARÂMETRO | OPERAÇÃO | PROJETO |
|---|---|---|
| PRESSÃO (bar g) | 8,0 | 11,0 |
| TEMPERATURA (°C) | 180 | 220 |
| TEMP. MÍNIMA (°C) | 20 | 0 |

| DADO | VALOR |
|---|---|
| FLUIDO | VP - VAPOR DE MÉDIA PRESSÃO |
| FASE / CATEG. FLUIDO | VAPOR / NORMAL |
| ESPEC. MATERIAL | B1A - AÇO CARBONO #150 RF |
| CÓDIGO DE PROJETO | ASME B31.3 |
| SOBRESPESSURA CORROSÃO | 1,6 mm |
| TESTE HIDROSTÁTICO | 16,5 bar g |
| ISOLAMENTO TÉRMICO | HC - CONSERV. CALOR 50 mm |
| TRAT. TÉRMICO (TTAT) | NÃO REQUERIDO |
| END SOLDAS | 100% VISUAL + 5% RT |
| PINTURA | ESQ. P-3 (ALTA TEMP.) |

### NOTAS

1. DIMENSÕES EM mm; COORDENADAS E ELEVAÇÕES EM m (LINHA DE CENTRO).
2. COMPRIMENTOS DE CORTE SEM ABERTURA DE RAIZ. TAKE-OFF CURVA RL = 229 mm.
3. FW-1: DEIXAR SOBREMETAL DE 100 mm NO SPOOL SP-01 P/ AJUSTE EM CAMPO.
4. FABRICAÇÃO, MONTAGEM E INSPEÇÃO CONFORME ASME B31.3 E ESPEC. B1A.
5. APERTO DE ESTOJOS CONFORME ASME PCC-1 (TORQUE CONTROLADO).

| REV | DATA | DESCRIÇÃO | POR | VERIF. | APROV. |
|---|---|---|---|---|---|
| 0 | 31/10/26 | EMISSÃO INICIAL - PARA CONSTRUÇÃO | EPF | RMS | JCL |

**PETROQUÍMICA MODELO S.A.**

ENGENHARIA DE TUBULAÇÃO - PROJETO 2026-045

TÍTULO

**ISOMÉTRICO DE TUBULAÇÃO**

LINHA 6"-VP-1001-B1A-HC  -  U-200 UTILIDADES

| DESENHO | VERIFICADO | APROVADO | DATA |
|---|---|---|---|
| EPF | RMS | JCL | 31/10/2026 |
| ESCALA | FORMATO | FOLHA | REF. P&ID |
| S/ ESCALA | A3 | 01 / 01 | DE-U200-003 |

| Nº DO DESENHO | REV. |
|---|---|
| ISO-U200-VP-1001-01 | 0 |